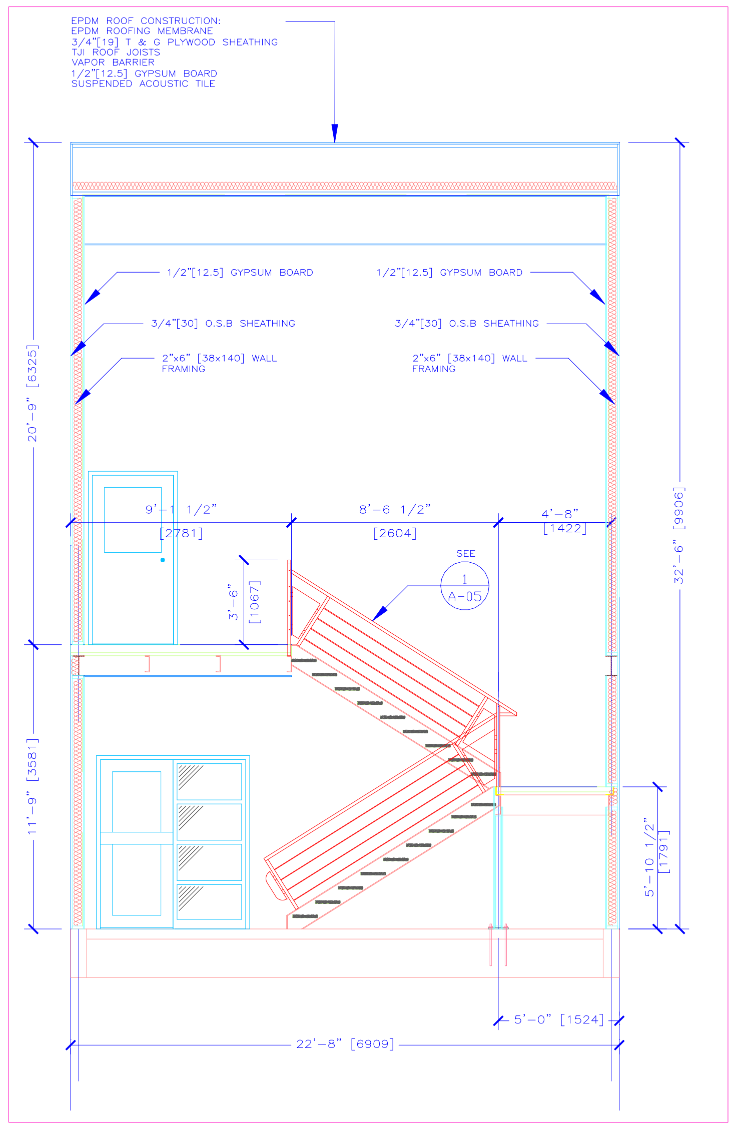

①STAIR SECTION 1
Scale:1/4" = 1'-0"

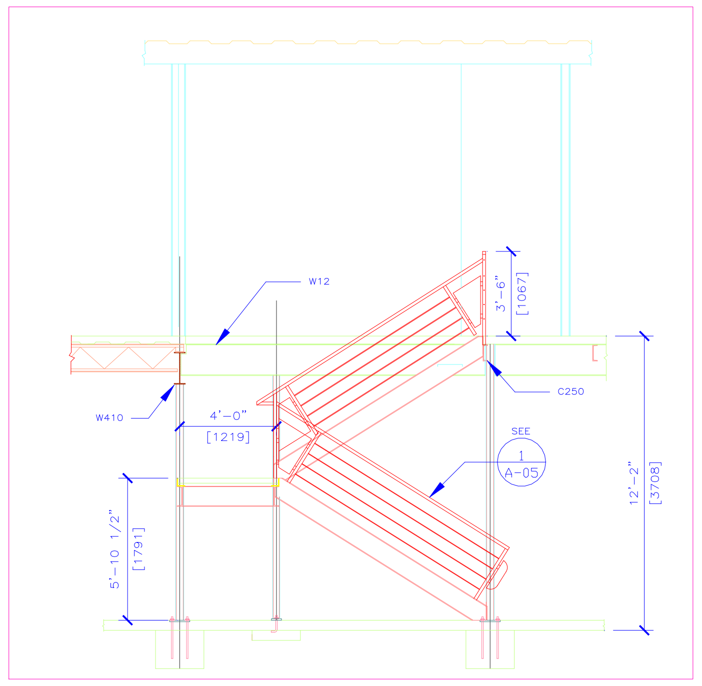

②STAIR SECTION 2
Scale:1/4" = 1'-0"

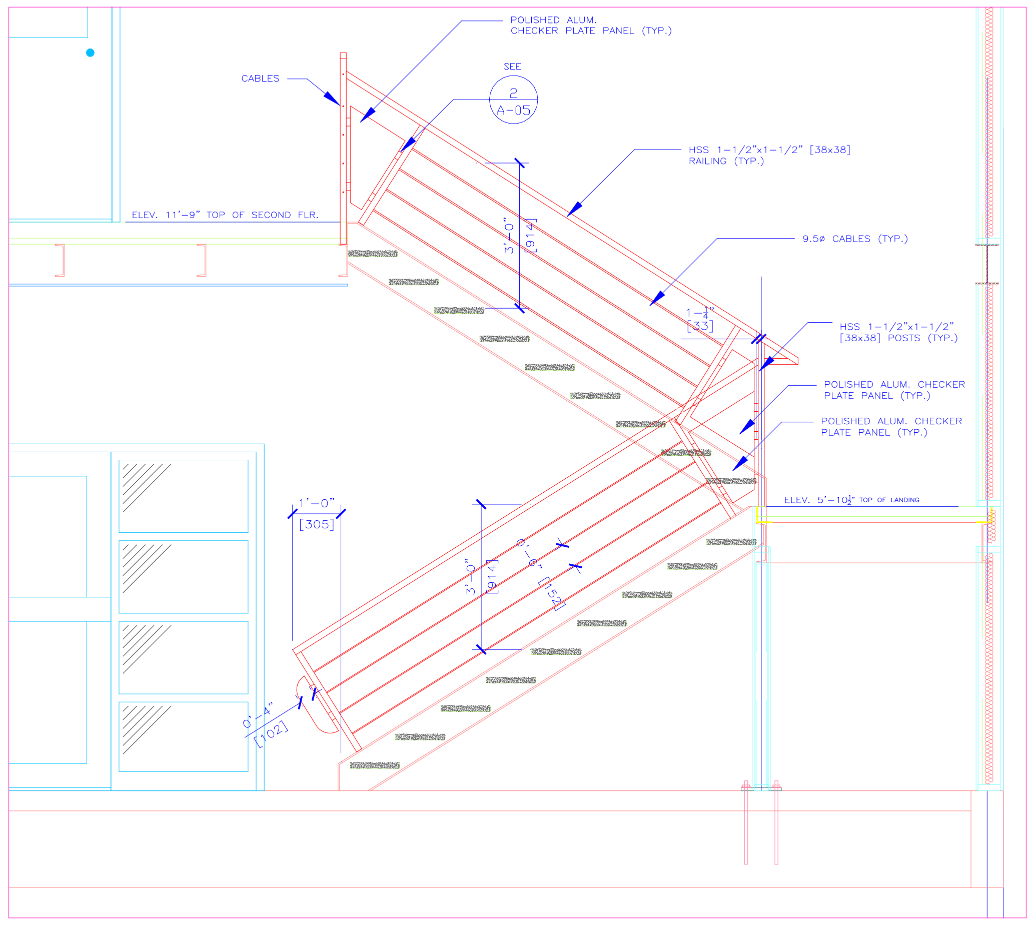
POLISHED ALUM. CHECKER PLATE PANEL (TYP.)
CABLES
SEE 2 A-05
HSS 1-1/2"x1-1/2" [38x38] RAILING (TYP.)
ELEV. 11'-9" TOP OF SECOND FLR.
3'-0" [914]
9.5ø CABLES (TYP.)
1-¼" [33]
HSS 1-1/2"x1-1/2" [38x38] POSTS (TYP.)
POLISHED ALUM. CHECKER PLATE PANEL (TYP.)
POLISHED ALUM. CHECKER PLATE PANEL (TYP.)
ELEV. 5'-10½" TOP OF LANDING
1'-0" [305]
3'-0" [914]
0'-6" [152]
0'-4" [102]

①STAIR DETAIL 1
Scale:1/2" = 1'-0"

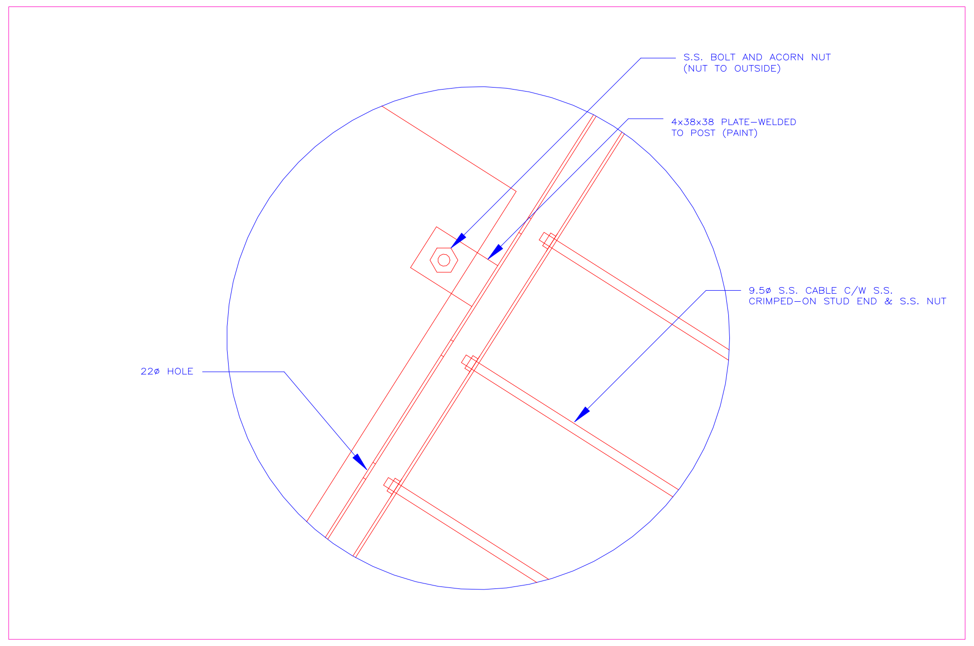
S.S. BOLT AND ACORN NUT (NUT TO OUTSIDE)
4x38x38 PLATE-WELDED TO POST (PAINT)
9.5ø S.S. CABLE C/W S.S. CRIMPED-ON STUD END & S.S. NUT
22ø HOLE

②STAIR DETAIL 2
Scale:3" = 1'-0"

JBS ENGINEERING INC.
CONSULTING ENGINEERS

SASKATOON SASKATCHEWAN

REV	REVISION	DATE
B	GENERAL REVISION	17/12/01
A	RELEASED FOR BLDG. PERMIT	20/11/01

revisions

project
INTERNATIONAL ROAD DYNAMICS
ADDITION – PHASE1
321 FIRST ST.
SASKATOON, SK 99999

client
ALLAN CONSTRUCTION LTD.
123 MAIN ST.
SASKATOON, SK 99999

content
STAIR SECTIONS
DETAILS

drawn by; NWP
checked by; SR
date; JAN. 2003
drawing no.
A-05

Filename: Architectural – Annotation Scaling and Multileaders.dwg Plotted: 12/5/2006 11:15:39 AM Plot Device: DWF6 EPlot.pc3 Page Setup: ---- Plotted by: Autodesk